
**SUPPLY SCOPE: Nudura ICF forms, accessories, pre-cut service, alignment hire and haulage as the quotation. ENGLAND - Building Regulations (LABC). 3rd-floor FFL ~8.23 m above the ground floor, below 11 m. 4 storeys incl. the attic (LABC warranty cap 3 - provider to confirm); Class 2A ties by the engineer. Precast floors, steels / transfer beams, roof structure, windows and timber partitions are shown in good faith for coordination only - engineer / specialists to design.**

**QUOTATION - NOT FOR CONSTRUCTION**

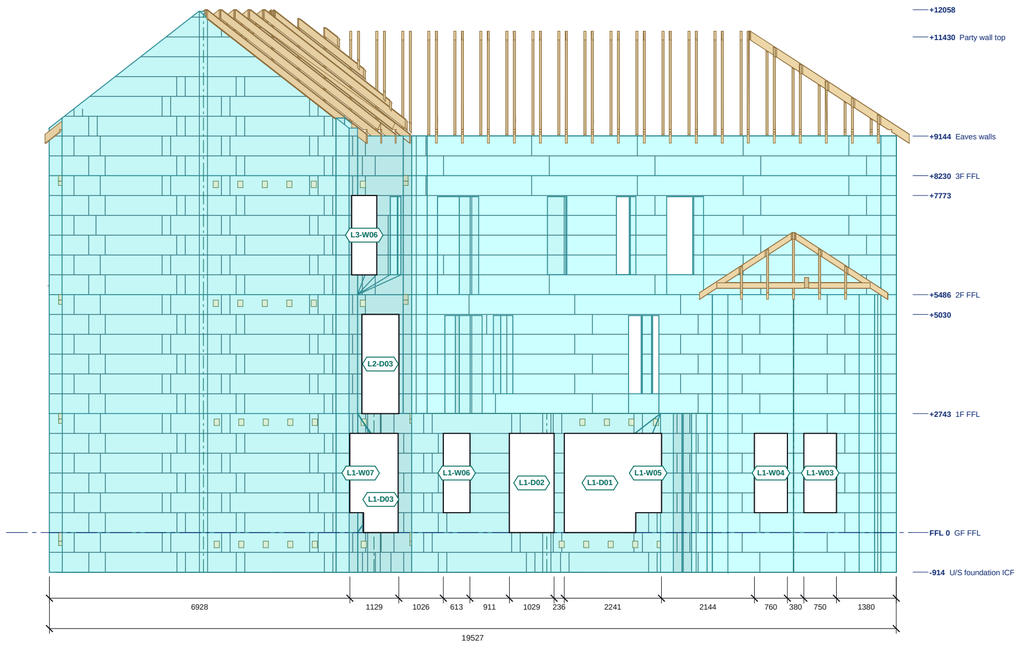


## NORTH ELEVATION

Scale 1:100 @ A2 | Levels above GF FFL; sills and heads in the schedule




## SOUTH ELEVATION

Scale 1:100 @ A2 | Levels above GF FFL; sills and heads in the schedule

ICF external EPS face
Block course joint
Stack joint

0 1 2 3 4 5m

Do not scale. All dimensions in millimetres, levels in metres from GF FFL. Check all dimensions on site.

## ELEVATION SCHEDULES

### NORTH ELEVATION: OPENINGS

| Ref | Width | Height | Sill | Head | Lintel |
|---|---|---|---|---|---|
| L1-W03 | 750 | 1829 | +457 | +2286 | - |
| L1-W04 | 760 | 1829 | +457 | +2286 | - |
| L1-W05 | 500 | 1829 | +457 | +2286 | - |
| L1-D01 | 1740 | 2286 | 0 | +2286 | - |
| L1-D02 | 1000 | 2286 | 0 | +2286 | - |
| L1-W07 | 360 | 1829 | +457 | +2286 | - |
| L1-D03 | 900 | 2286 | 0 | +2286 | - |
| L1-W06 | 500 | 1829 | +457 | +2286 | - |
| L2-D03 | 1000 | 2286 | +2743 | +5029 | - |
| L3-W06 | 510 | 1829 | +5944 | +7772 | - |

Structural openings in the ICF; sill and head above GF FFL.

### SOUTH ELEVATION: OPENINGS

| Ref | Width | Height | Sill | Head | Lintel |
|---|---|---|---|---|---|
| L1-W12 | 900 | 1829 | +457 | +2286 | - |
| L1-D04 | 900 | 2286 | 0 | +2286 | - |
| L1-W18 | 910 | 1829 | +457 | +2286 | - |
| L1-W11 | 400 | 1829 | +457 | +2286 | - |
| L1-W17 | 400 | 1829 | +457 | +2286 | - |
| L1-W13 | 400 | 1829 | +457 | +2286 | - |
| L1-W19 | 400 | 1829 | +457 | +2286 | - |
| L1-W14 | 600 | 1829 | +457 | +2286 | - |
| L1-W15 | 680 | 1829 | +457 | +2286 | - |
| L1-W16 | 680 | 1829 | +457 | +2286 | - |
| L1-W10 | 400 | 1829 | +457 | +2286 | - |
| L1-W09 | 910 | 1829 | +457 | +2286 | - |
| L2-W10 | 900 | 1829 | +3200 | +5029 | - |
| L2-W13 | 900 | 1829 | +3200 | +5029 | - |
| L2-W17 | 910 | 1829 | +3200 | +5029 | - |
| L2-W09 | 400 | 1829 | +3200 | +5029 | - |
| L2-W16 | 400 | 1829 | +3200 | +5029 | - |
| L2-W11 | 400 | 1829 | +3200 | +5029 | - |
| L2-W18 | 400 | 1829 | +3200 | +5029 | - |
| L2-W12 | 600 | 1829 | +3200 | +5029 | - |
| L2-W14 | 680 | 1829 | +3200 | +5029 | - |
| L2-W15 | 680 | 1829 | +3200 | +5029 | - |
| L2-W08 | 400 | 1829 | +3200 | +5029 | - |
| L2-W07 | 910 | 1829 | +3200 | +5029 | - |
| L3-W11 | 750 | 1829 | +5944 | +7772 | - |
| L3-W14 | 740 | 1829 | +5944 | +7772 | - |
| L3-W15 | 750 | 1829 | +5944 | +7772 | - |
| L3-W09 | 750 | 1372 | +6401 | +7772 | - |

Structural openings in the ICF; sill and head above GF FFL.

### NORTH ELEVATION: LEVELS

| Level | FFL |
|---|---|
| U/S foundation ICF | -914 |
| GF FFL | 0 |
| 1F FFL | +2743 |
| top of ICF | +5030 |
| 2F FFL | +5486 |
| top of ICF | +7773 |
| 3F FFL | +8230 |
| Eaves walls | +9144 |
| Party wall top | +11430 |
| top of roof build-up | +12058 |

### SOUTH ELEVATION: LEVELS

| Level | FFL |
|---|---|
| U/S foundation ICF | -914 |
| GF FFL | 0 |
| top of ICF | +2286 |
| 1F FFL | +2743 |
| top of ICF | +5030 |
| 2F FFL | +5486 |
| top of ICF | +7773 |
| 3F FFL | +8230 |
| Eaves walls | +9144 |
| Party wall top | +11430 |
| top of roof build-up | +12058 |

### NOTES

1. ICF: Nudura 6" XR35, 101.6 EPS + 152.4 core + 101.6 EPS = 355.6; 6" Std, 66.7 EPS + 152.4 core + 66.7 EPS = 285.8. External EPS face shown with the block course joints, vertical block joints and stack joints as populated.
2. Levels above GF FFL. Openings are structural openings in the ICF; glazing, doors, render and finishes by others, not shown.
3. Masonry shown as modelled.
4. See ES26-087-GA-01 for plan setting out, lintels and steel.

### REVISIONS

| REV | DATE | DESCRIPTION |
|---|---|---|
| - | 02.11.26 | Quotation issue |

Nudura™ BuildEase

| CLIENT | PROJECT |
|---|---|
| JAUS (via Tremco CPG UK) | Bromfelde Corner, 25 Bromfelde Road, London SW4 6PP |

DRAWING TITLE
**NORTH AND SOUTH ELEVATIONS**

ICF elevations with openings, levels and roof build-up

| SCALE | SIZE | DATE |
|---|---|---|
| 1:100 | A2 | 02.11.26 |
| DRAWN | CHECKED | APPROVED |
| TS | | |

| STATUS | DRAWING No. | REV |
|---|---|---|
| QUOTATION | ES26-087-EL-01 | - |