
SUPPLY SCOPE: Nudura ICF forms, accessories, pre-cut service, alignment hire and haulage as the quotation. ENGLAND - Building Regulations (LABC). 3rd-floor FFL ~8.23 m above the ground floor, below 11 m. 4 storeys incl. the attic (LABC warranty cap 3 - provider to confirm); Class 2A ties by the engineer. Precast floors, steels / transfer beams, roof structure, windows and timber partitions are shown in good faith for coordination only - engineer / specialists to design.

QUOTATION - NOT FOR CONSTRUCTION

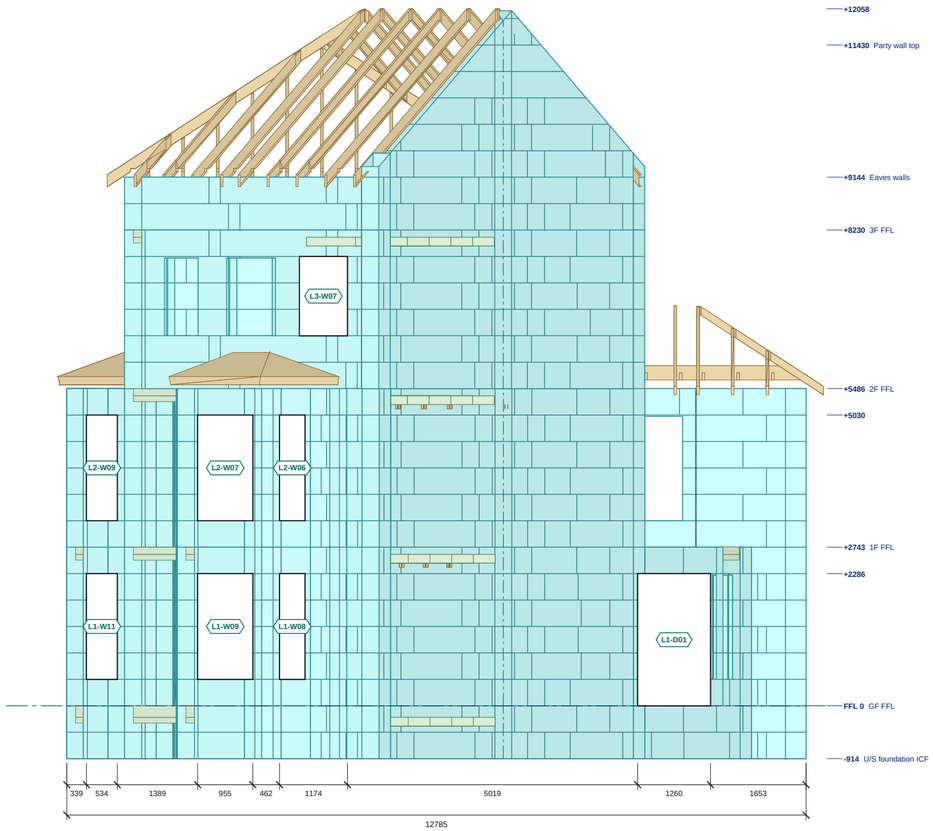

EAST ELEVATION

Scale 1:75 @ A2 | Levels above GF FFL; sills and heads in the schedule



WEST ELEVATION

Scale 1:75 @ A2 | Levels above GF FFL; sills and heads in the schedule

ICF external EPS face
Block course joint
Stack joint

0 1 2 3 4m

ELEVATION SCHEDULES

EAST ELEVATION: OPENINGS

Ref	Width	Height	Sill	Head	Lintel
L1-W08	340	1829	+457	+2286	-
L1-W09	910	1829	+457	+2286	-
L1-W11	400	1829	+457	+2286	-
L1-D01	1740	2286	0	+2286	-
L2-W06	340	1829	+3200	+5029	-
L2-W07	910	1829	+3200	+5029	-
L2-W09	400	1829	+3200	+5029	-
L3-W07	760	1372	+6401	+7772	-

Structural openings in the ICF; sill and head above GF FFL.

WEST ELEVATION: OPENINGS

Ref	Width	Height	Sill	Head	Lintel
L1-W01	500	1829	+457	+2286	-
L1-W02	500	1829	+457	+2286	-
L1-W19	400	1829	+457	+2286	-
L2-W01	500	1829	+3200	+5029	-
L2-W02	500	1829	+3200	+5029	-
L2-W03	1000	1829	+3200	+5029	-
L2-W18	400	1829	+3200	+5029	-
L3-W01	500	1829	+5944	+7772	-
L3-W02	500	1829	+5944	+7772	-
L3-W05	500	1829	+5944	+7772	-
L3-W06	510	1829	+5944	+7772	-

Structural openings in the ICF; sill and head above GF FFL.

EAST ELEVATION: LEVELS

Level	FFL
U/S foundation ICF	-914
GF FFL	0
top of ICF	+2286
1F FFL	+2743
top of ICF	+5030
2F FFL	+5486
3F FFL	+8230
Eaves walls	+9144
Party wall top	+11430
top of roof build-up	+12058

WEST ELEVATION: LEVELS

Level	FFL
U/S foundation ICF	-914
GF FFL	0
top of ICF	+2286
1F FFL	+2743
top of ICF	+5030
2F FFL	+5486
top of ICF	+7773
3F FFL	+8230
Eaves walls	+9144
Party wall top	+11430
top of roof build-up	+12058

NOTES

1. ICF: Nudura 6" XR35, 101.6 EPS + 152.4 core + 101.6 EPS = 355.6; 6" Std, 66.7 EPS + 152.4 core + 66.7 EPS = 285.8. External EPS face shown with the block course joints, vertical block joints and stack joints as populated.
2. Levels above GF FFL. Openings are structural openings in the ICF; glazing, doors, render and finishes by others, not shown.
3. Masonry shown as modelled.
4. See ES26-087-GA-01 for plan setting out, lintels and steel.

REVISIONS

REV	DATE	DESCRIPTION
-	02.11.26	Quotation issue

Nudura™ BuildEase

CLIENT	PROJECT
JAUS (via Tremco CPG UK)	Bromfelde Corner, 25 Bromfelde Road, London SW4 6PP

DRAWING TITLE

EAST AND WEST ELEVATIONS

ICF elevations with openings, levels and roof build-up

SCALE	SIZE	DATE
1:75	A2	02.11.26
DRAWN	CHECKED	APPROVED
TS		

STATUS	DRAWING No.	REV
QUOTATION	ES26-087-EL-02	-

Do not scale. All dimensions in millimetres, levels in metres from GF FFL. Check all dimensions on site.