
SUPPLY SCOPE: Nudura ICF forms, accessories, pre-cut service, alignment hire and haulage as the quotation. ENGLAND - Building Regulations (LABC). 3rd-floor FFL ~8.23 m above the ground floor, below 11 m. 4 storeys incl. the attic (LABC warranty cap 3 - provider to confirm); Class 2A ties by the engineer. Precast floors, steels / transfer beams, roof structure, windows and timber partitions are shown in good faith for coordination only - engineer / specialists to design.

QUOTATION - NOT FOR CONSTRUCTION

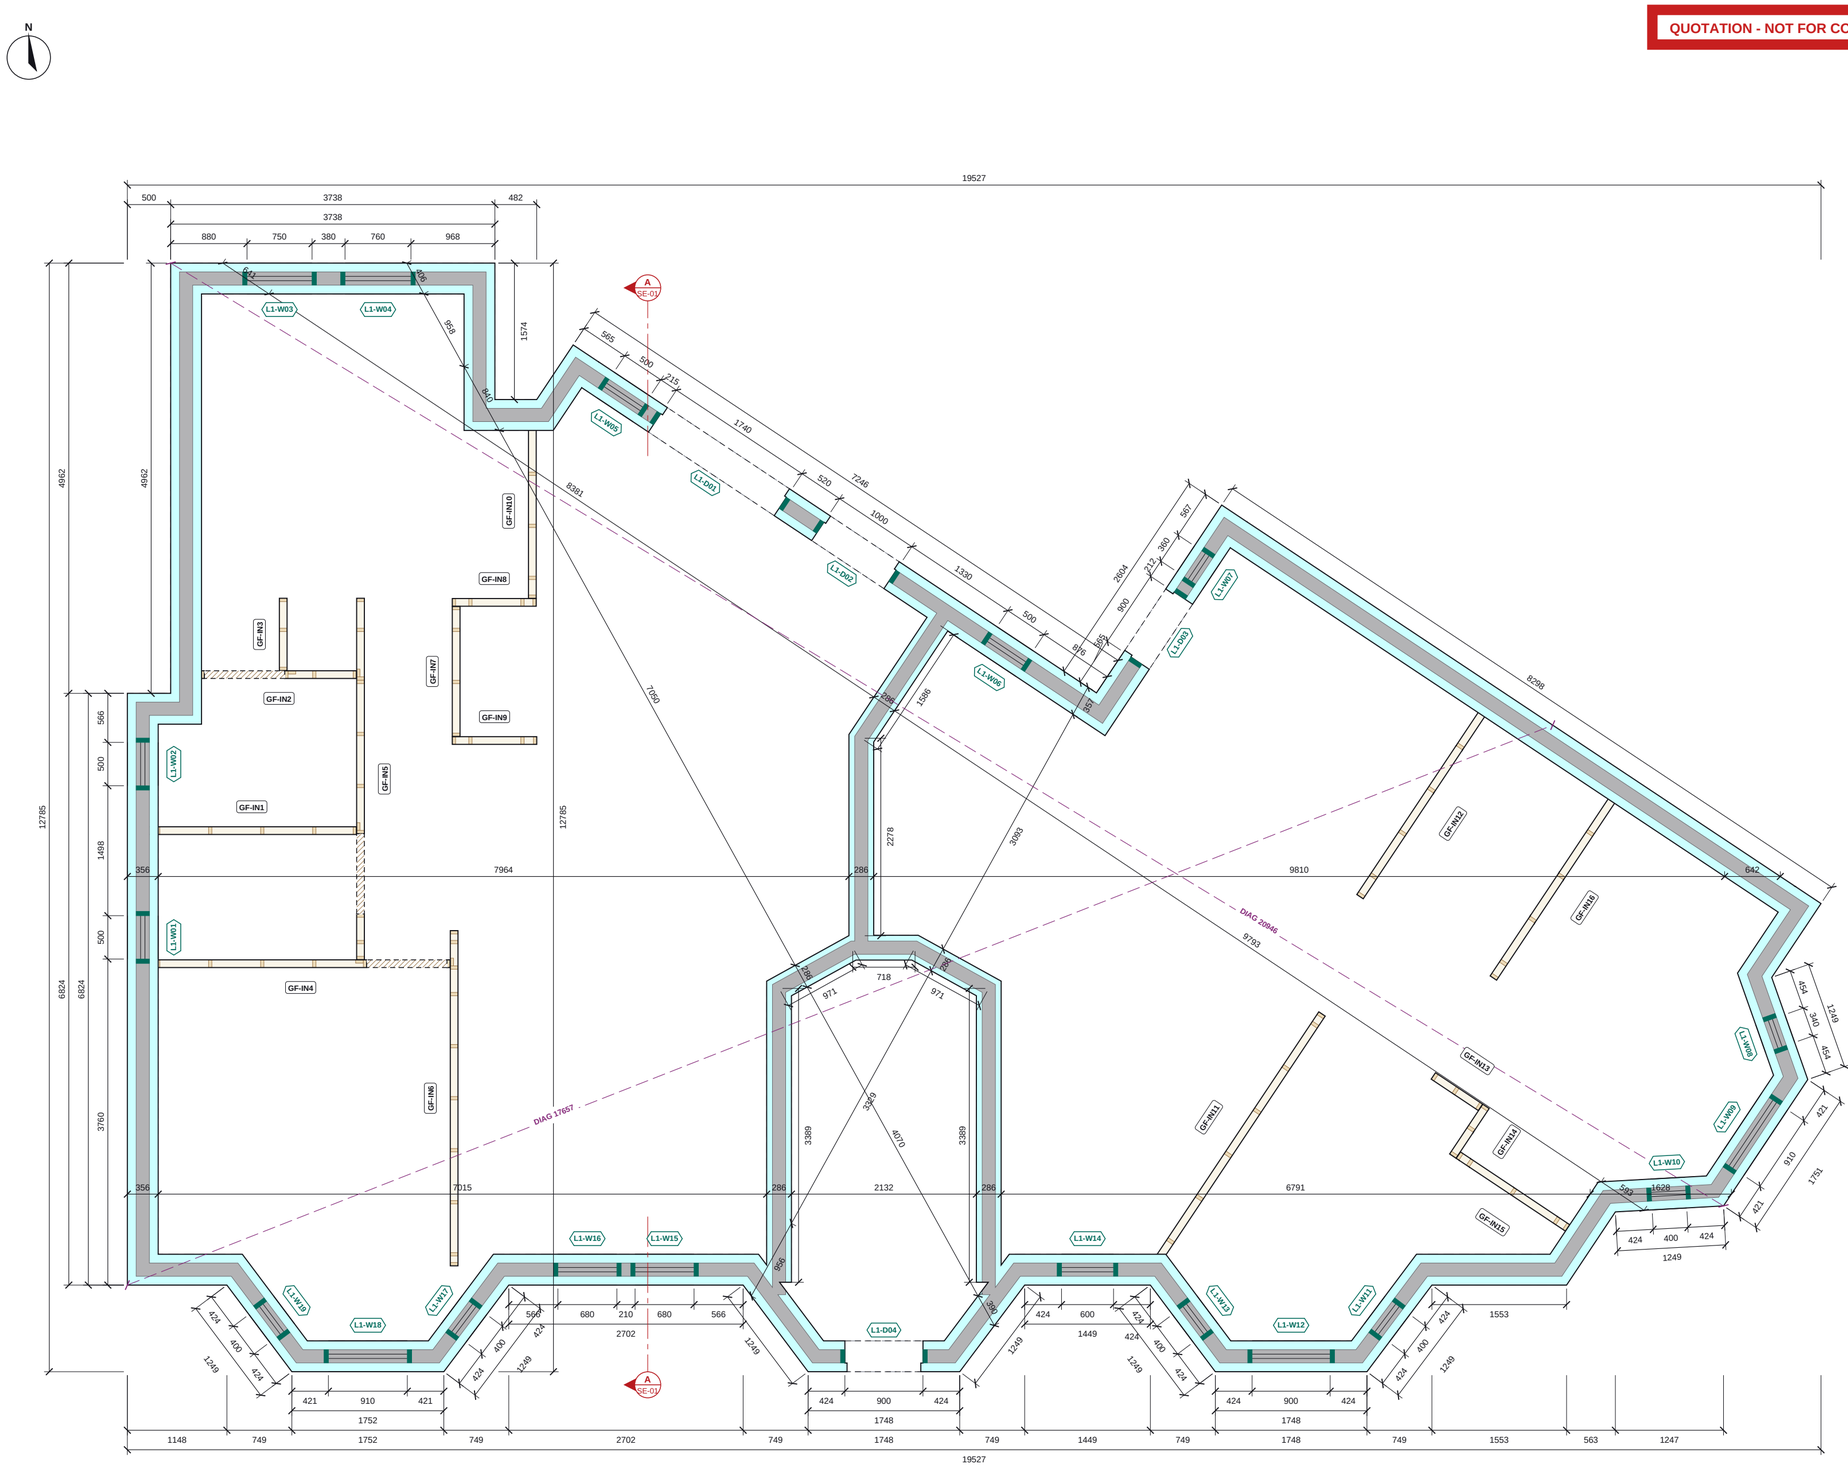

GROUND FLOOR ICF PLAN

Scale 1:50 @ A2 | Plan cut at +400

0 1 2 3m

GROUND FLOOR ICF SCHEDULES

OPENING SCHEDULE

Ref	Width	Height	Sill	Head	Lintel
L1-W01	500	1829	+457	+2286	-
L1-W02	500	1829	+457	+2286	-
L1-W03	750	1829	+457	+2286	-
L1-W04	760	1829	+457	+2286	-
L1-W05	500	1829	+457	+2286	-
L1-D01	1740	2286	0	+2286	-
L1-D02	1000	2286	0	+2286	-
L1-W06	500	1829	+457	+2286	-
L1-D03	900	2286	0	+2286	-
L1-W07	360	1829	+457	+2286	-
L1-W09	910	1829	+457	+2286	-
L1-W10	400	1829	+457	+2286	-
L1-W11	400	1829	+457	+2286	-
L1-W12	900	1829	+457	+2286	-
L1-W13	400	1829	+457	+2286	-
L1-W14	600	1829	+457	+2286	-
L1-D04	900	2286	0	+2286	-
L1-W17	400	1829	+457	+2286	-
L1-W18	910	1829	+457	+2286	-
L1-W19	400	1829	+457	+2286	-
L1-W08	340	1829	+457	+2286	-
L1-W15	680	1829	+457	+2286	-
L1-W16	680	1829	+457	+2286	-

Structural openings in the ICF; sill and head above GF FFL.

NOTES

1. ICF: Nudura 6" XR35, 101.6 EPS + 152.4 core + 101.6 EPS = 355.6; 6" Std, 66.7 EPS + 152.4 core + 66.7 EPS = 285.8. Dimensions to the ICF faces.
2. Levels above GF FFL. Sill / head = structural opening in the ICF.
3. No structural design yet (planning drawings). ICF per the quotation model: 6in XR35 external walls and foundation (2 courses on a strip footing), 6in Std separating walls (stair core + flat separating walls). Precast floors bear on the ICF core; transfer beams under the 1F north wall and the wing east wall, the indicative steels and the Class 2A ties for the engineer.
4. Lintel (L-n) and steel (B-n, C-1) marks from rev -, which takes precedence.
5. Masonry walls shown for context.

REVISIONS

REV	DATE	DESCRIPTION
-	02.11.26	Quotation issue

Nudura™ BuildEase

CLIENT	PROJECT
JAUS (via Tremco CPG UK)	Bromfelde Corner, 25 Bromfelde Road, London SW4 6PP

DRAWING TITLE
GROUND FLOOR ICF GENERAL ARRANGEMENT
ICF walls, openings, lintels, steel over and engineer's notes

SCALE	SIZE	DATE
1:50	A2	02.11.26
DRAWN	CHECKED	APPROVED
TS		

STATUS	DRAWING No.	REV
QUOTATION	ES26-087-GA-02	-

Do not scale. All dimensions in millimetres, levels in metres from GF FFL. Check all dimensions on site.