
SUPPLY SCOPE: Nudura ICF forms, accessories, pre-cut service, alignment hire and haulage as the quotation. ENGLAND - Building Regulations (LABC). 3rd-floor FFL ~8.23 m above the ground floor, below 11 m. 4 storeys incl. the attic (LABC warranty cap 3 - provider to confirm); Class 2A ties by the engineer. Precast floors, steels / transfer beams, roof structure, windows and timber partitions are shown in good faith for coordination only - engineer / specialists to design.

QUOTATION - NOT FOR CONSTRUCTION

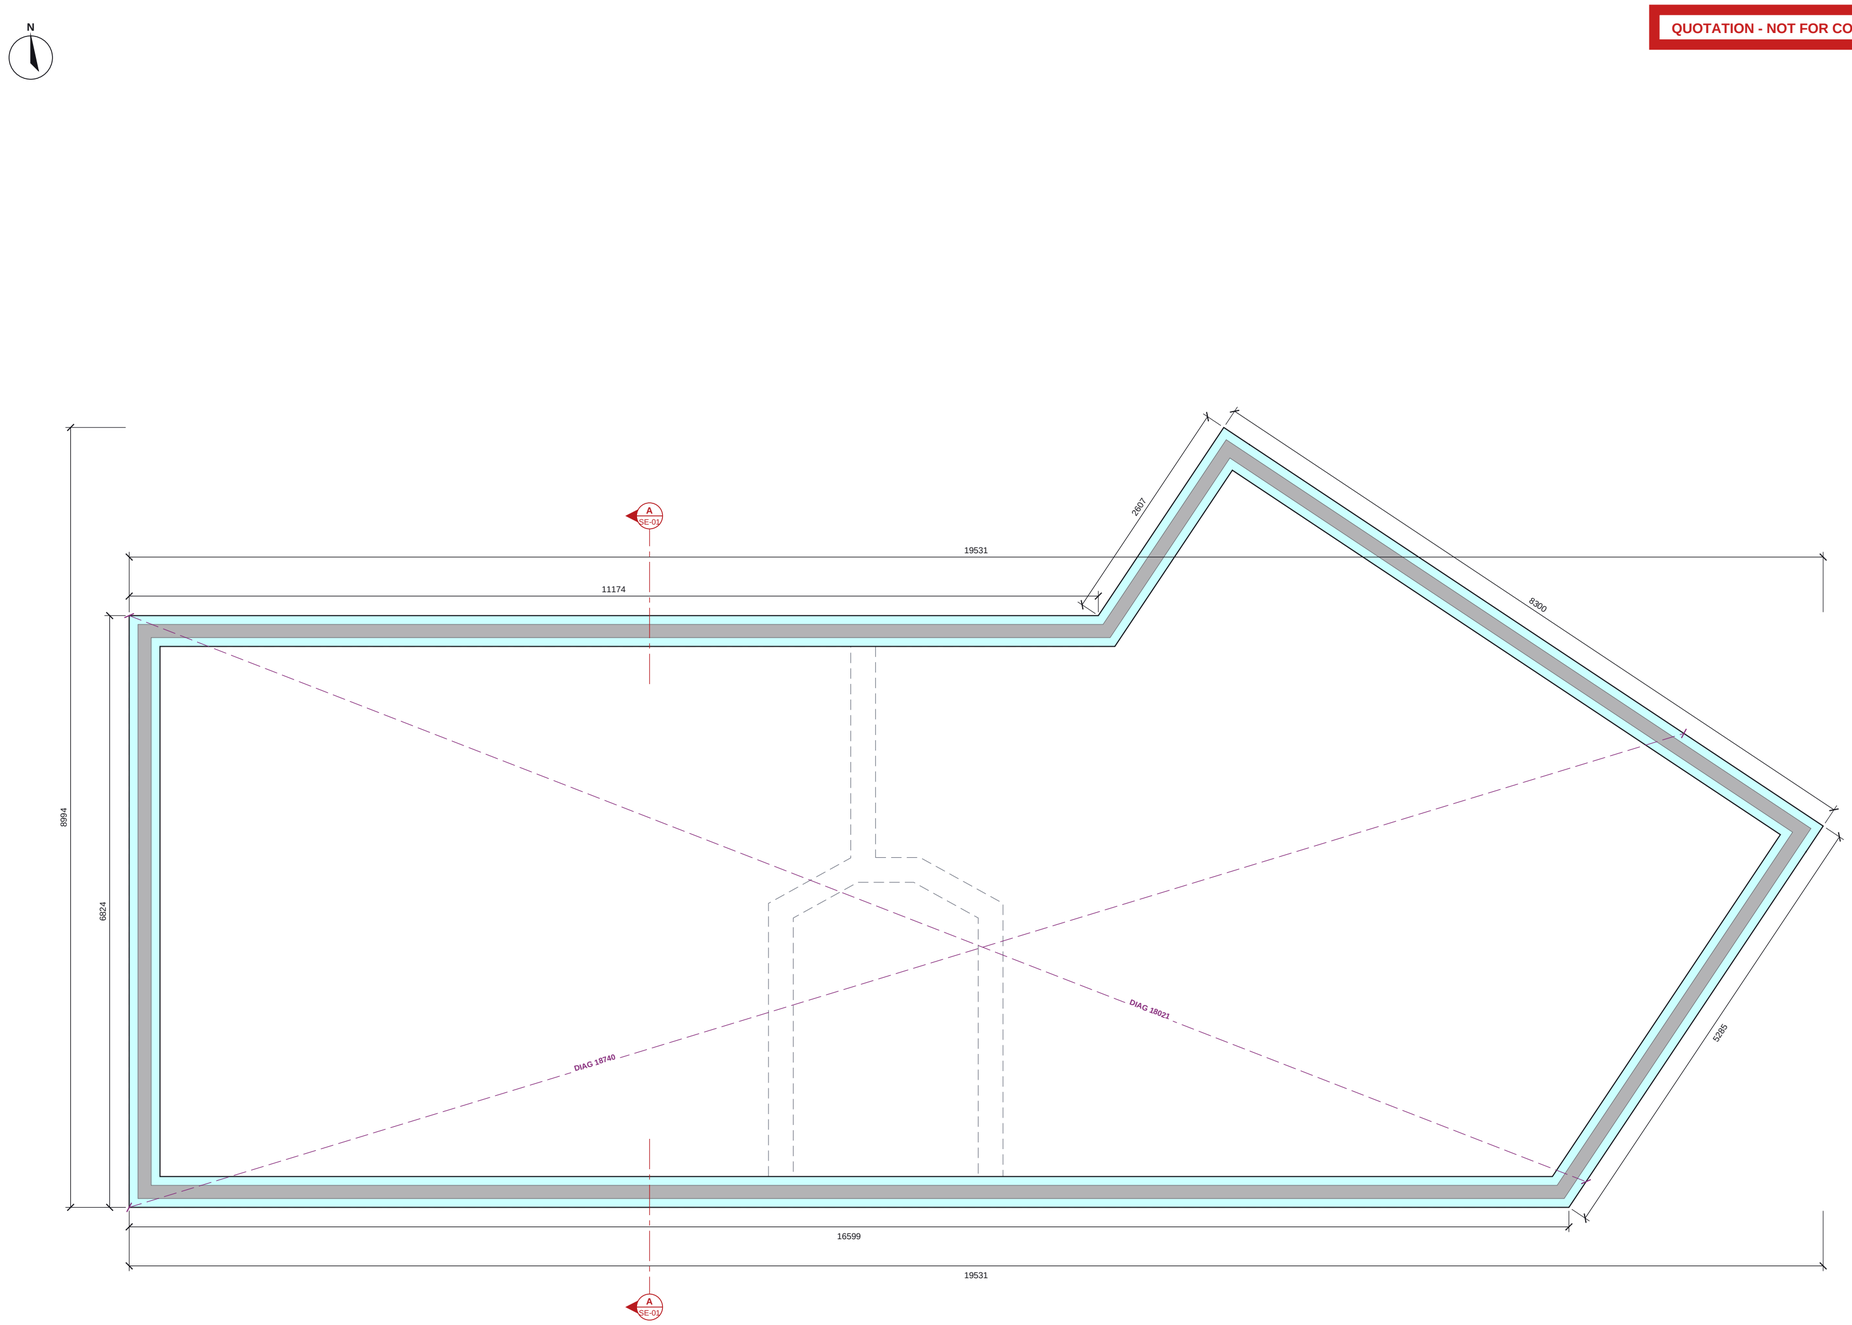

- EPS insulation (Nudura form)
- Concrete core
- End cap at opening
- Load-bearing masonry wall (context)
- Timber frame partition panel, studs cut at plan level
- Panel joint
- Door opening in a timber partition (hatched through the door, head over dashed)
- ICF walls of the level below (dashed)
- Engineer's pier bars (n-H12 vertical bars in ICF pier) / WS wall starters
- Setting-out check diagonal (external ICF corners)
- Section line (see SE sheet)

THIRD FLOOR (EAVES + NE PARTY WALL) ICF PLAN

Scale 1:50 @ A2 | Plan cut at +9130

0 1 2 3m

THIRD FLOOR (EAVES + NE PARTY WALL) ICF SCHEDULES

OPENING SCHEDULE

Ref	Width	Height	Sill	Head	Lintel
none					

Structural openings in the ICF; sill and head above GF FFL.

NOTES

1. ICF: Nudura 6" XR35, 101.6 EPS + 152.4 core + 101.6 EPS = 355.6. Dimensions to the ICF faces.
2. Levels above GF FFL. Sill / head = structural opening in the ICF.
3. No structural design yet (planning drawings). ICF per the quotation model: 6in XR35 external walls and foundation (2 courses on a strip footing), 6in Std separating walls (stair core + flat separating walls). Precast floors bear on the ICF core; transfer beams under the 1F north wall and the wing east wall, the indicative steels and the Class 2A ties for the engineer.
4. Lintel (L-n) and steel (B-n, C-1) marks from rev -, which takes precedence.
5. Masonry walls shown for context.

REVISIONS

REV	DATE	DESCRIPTION
-	02.11.26	Quotation issue

Nudura™ BuildEase

CLIENT	PROJECT
JAUS (via Tremco CPG UK)	Bromfelde Corner, 25 Bromfelde Road, London SW4 6PP

DRAWING TITLE
THIRD FLOOR (EAVES + NE PARTY WALL) ICF GENERAL ARRANGEMENT

SCALE	SIZE	DATE
1:50	A2	02.11.26
DRAWN	CHECKED	APPROVED
TS		

STATUS	DRAWING No.	REV
QUOTATION	ES26-087-GA-05	-

Do not scale. All dimensions in millimetres, levels in metres from GF FFL. Check all dimensions on site.