
SUPPLY SCOPE: Nudura ICF forms, accessories, pre-cut service, alignment hire and haulage as the quotation. ENGLAND - Building Regulations (LABC). 3rd-floor FFL ~8.23 m above the ground floor, below 11 m. 4 storeys incl. the attic (LABC warranty cap 3 - provider to confirm); Class 2A ties by the engineer. Precast floors, steels / transfer beams, roof structure, windows and timber partitions are shown in good faith for coordination only - engineer / specialists to design.

QUOTATION - NOT FOR CONSTRUCTION

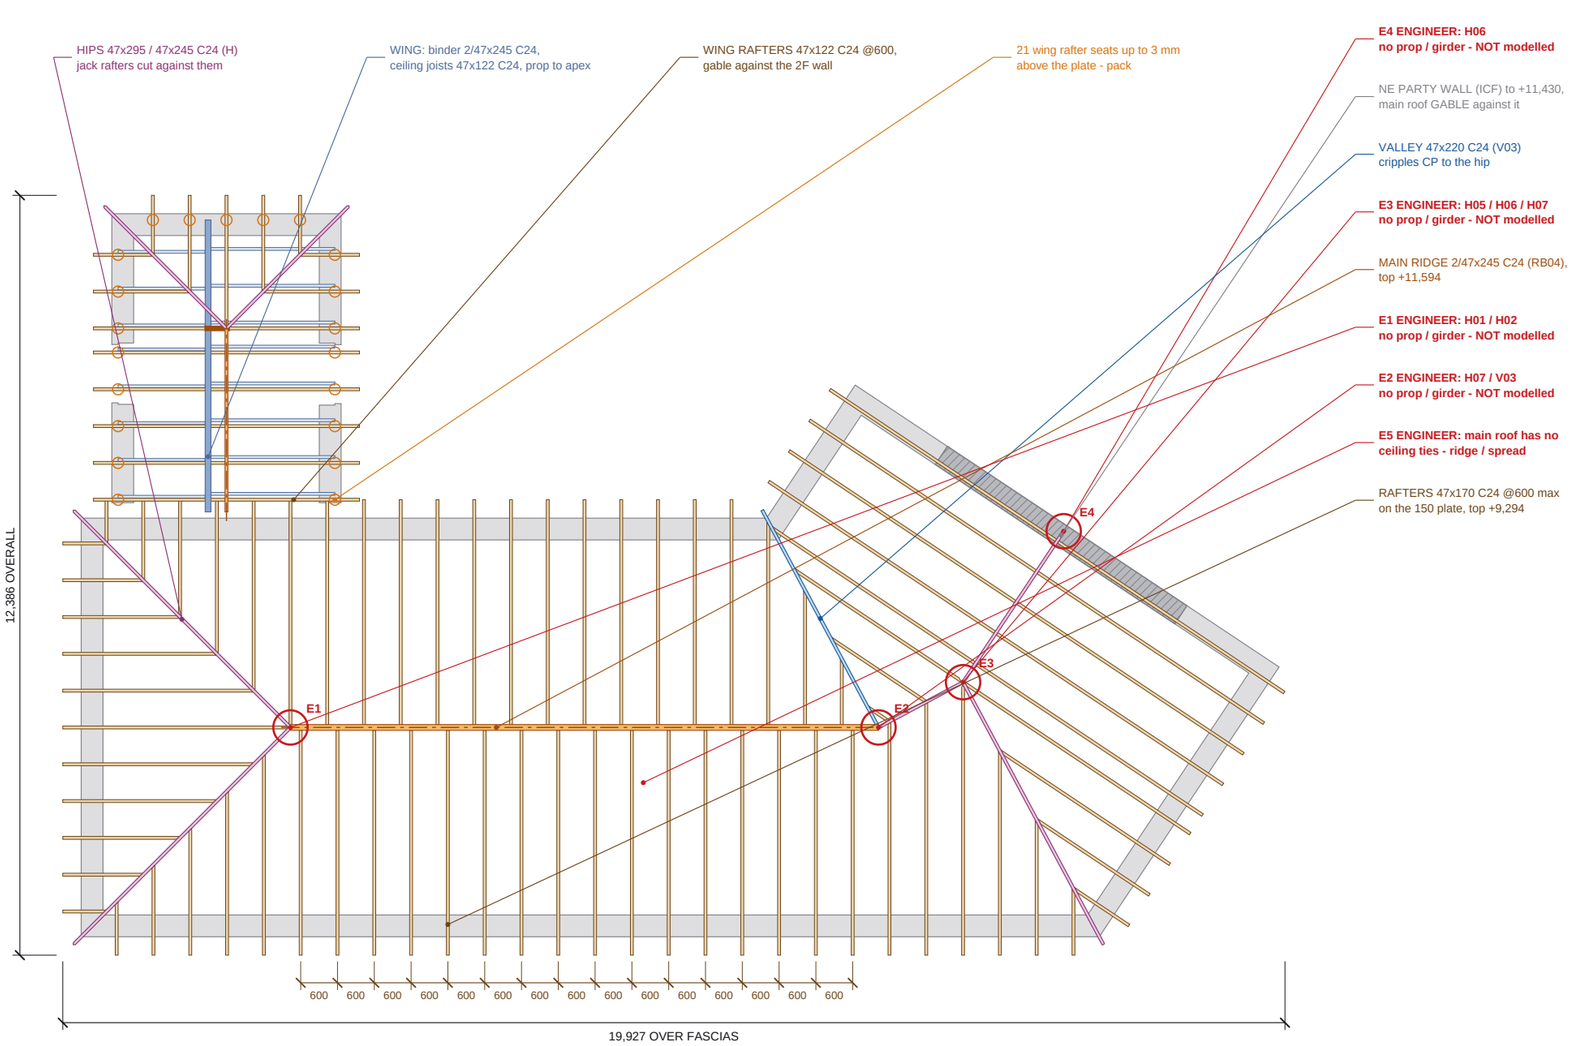

SOUTH (Bromfelde Road front)

Rafter / jack / cripple
Ridge board / prop
NE party wall above the eaves (to +11,430)
Wing seat above the plate (pack)
Hip rafter
Ceiling joist / binder (wing)
ICF eaves walls (main +9,000, wing +5,000)
Valley rafter
Ridge line
ENGINEER item (not modelled)

ROOF STRUCTURE PLAN

Scale 1:100 @ A3 | Plan on the rafters, slates / battens / membrane omitted

0 1 2 3 4 5m

ROOF STRUCTURE SCHEDULES

ROOF MEMBER SCHEDULE

Roof	Mark	Member	Section	Length	Qty
Main	RB	Ridge board	2/47x245 C24	9,588	1
Main	H	Hip rafter	47x245 C24	1,635-5,816	3
Main	H	Hip rafter	47x295 C24	5,777	2
Main	V	Valley rafter	47x220 C24	4,852	1
Main	R	Common rafter	47x170 C24	4,426	29
Main	CR	Crown rafter (hip end)	47x170 C24	4,426-5,306	2
Main	JH	Jack rafter, plate -> hip	47x170 C24	849-5,306	38
Main	JV	Jack rafter, valley -> ridge	47x170 C24	1,335-4,005	3
Main	CP	Cripple, valley -> hip	47x170 C24	512-4,761	4
Wing	RB	Ridge board	47x195 C16	2,991	1
Wing	H	Hip rafter	47x170 C24	3,375	2
Wing	R	Common rafter	47x122 C24	2,586	12
Wing	CR	Crown rafter (hip end)	47x122 C24	2,586	1
Wing	JH	Jack rafter, plate -> hip	47x122 C24	1,155-1,871	8
Wing	BN	Binder (ceiling joists hang off it)	2/47x245 C24	4,758	1
Wing	CJ	Ceiling joist	47x122 C24	1,419-2,019	16
Wing	P	Raking prop, binder -> apex	75x97 C24	916	1
		Total members			**125**

Lengths = cut lengths from the model (min-max where the members vary). 2/.. = 2-ply. Marks are the model id prefixes.

ROOF METALWORK

Item	Main	Wing
TCP47 rafter clip to the wall plate	69	21
Joist hanger (ceiling joists to the binder)	-	16

NOTES

1. MAIN roof as modelled for the quotation (TLS roof framer, cut roof): hipped, 33 deg, GABLE against the NE party wall (party wall up to +11,430). Rafters 47x170 C24 @600 max, hips 47x245 C24 / 47x295 C24, valley 47x220 C24, ridge 2/47x245 C24; seated on the 150 wall plate on the ICF core of the eaves walls (plate top +9,294).
2. WING roof (two-storey wing): hipped, 33 deg, GABLE against the 2F wall of the main block. Rafters 47x122 C24 @600, hips 47x170 C24, ridge board 47x195 C16; 16 No. 47x122 C24 ceiling joists on a 2/47x245 C24 binder with a 75x97 C24 raking prop to the apex; plate top ~+5,636.
3. Natural slate on battens / membrane (by others), C24 @600. Rafter seats on TCP47 clips to the plates (90 No., design uplift up to 0.65 kN), 16 joist hangers on the wing binder. Plate holding-down straps to the engineer.
4. ENGINEER ITEMS - NOT MODELLED (FormFramer load path, no invented posts / beams; red rings): (E1) H01 hip head: no prop / girder under it; H02 hip head: no prop / girder under it. (E2) H07 hip foot on the plate; V03 valley head: no prop / girder under it. (E3) H05 hip head: no prop / girder under it; H06 hip head: no prop / girder under it; H07 hip head: no prop / girder under it. (E4) H06 hip foot on the plate. (E5) MAIN ROOF HAS NO CEILING TIES (attic over the 3F precast floor): ridge 2/47x245 C24 spans between the unsupported apexes. Structural ridge / girders / props, bearings and rafter-spread restraint to the engineer.
5. WING: 21 rafter seats sit up to 3 mm above the plate (planes' heel vs rafter depth) - pack the seats or re-apply the heel at construction issue.
6. INDICATIVE - ENGLAND (London SW4), Building Regulations (LABC): wind / snow loads, sizes and fixings to the engineer. Levels above GF FFL, mm.

REVISIONS

REV	DATE	DESCRIPTION
-	02.11.26	Quotation issue

Nudura™ BuildEase

CLIENT	PROJECT
JAUS (via Tremco CPG UK)	Bromfelde Corner, 25 Bromfelde Road, London SW4 6PP

DRAWING TITLE
ROOF STRUCTURE

Main + wing cut roofs: rafters, hips, valley, ridges, ceiling joists, binder

SCALE	SIZE	DATE
1:100	A3	02.11.26
DRAWN	CHECKED	APPROVED
TS		

STATUS	DRAWING No.	REV
QUOTATION	ES26-087-RF-01	-

Do not scale. All dimensions in mm. Check all dimensions on site.